


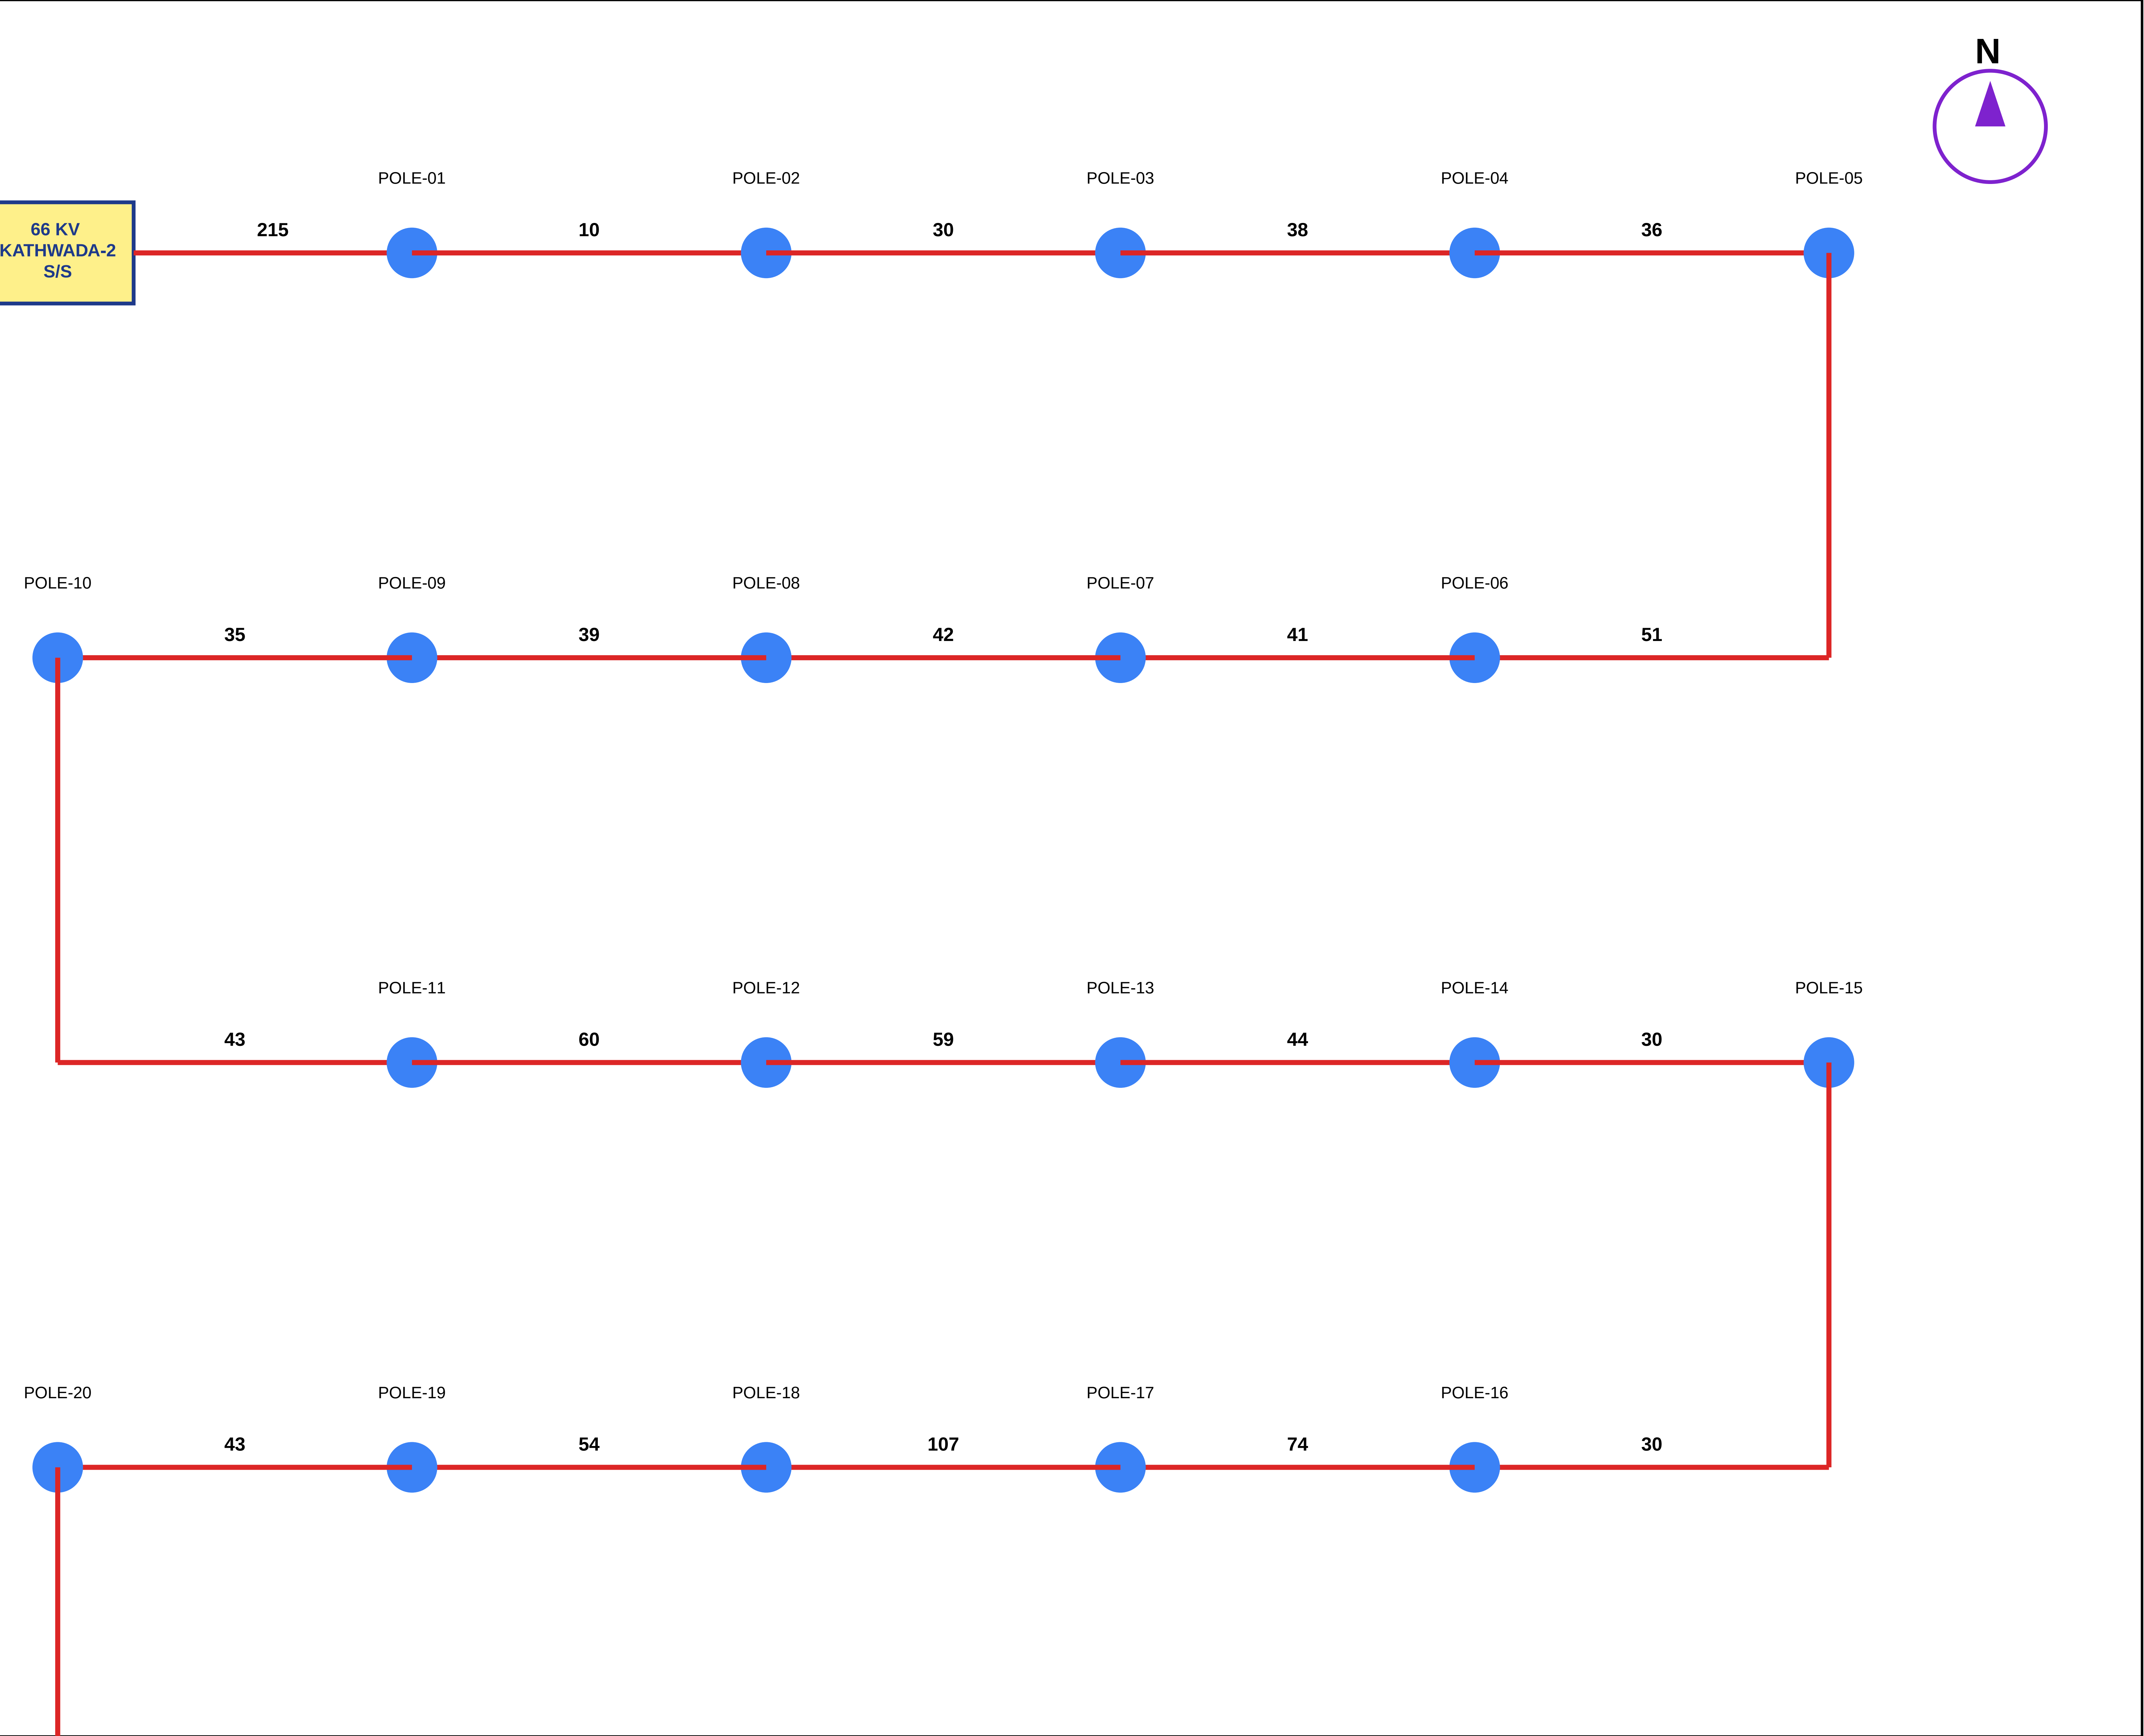

NAME OF CIRCLE: ANJAR-CIRCLE	FEEDER: JOGNINATH	11KV (OH TO UG) JOGNINATH FEEDER SINGLE LINE DIAGRAM (SLD)
NAME OF DIVISION: ANJAR-DIVISION	LOCATION: KATHWADA	
NAME OF SUB-DIVISION: AADIPUR-SUB	FROM S/S: KATHWADA-2	

NAME OF CIRCLE: ANJAR-CIRCLE	FEEDER: JOGNINATH	11KV (OH TO UG) JOGNINATH FEEDER SINGLE LINE DIAGRAM (SLD)
NAME OF DIVISION: ANJAR-DIVISION	LOCATION: KATHWADA	
NAME OF SUB-DIVISION: AADIPUR-SUB	FROM S/S: KATHWADA-2	



LEGENDS		
DESCRIPTION	SYMBOL / QTY	
FEEDER		
JOGNINATH		
CABLE LENGTH SUMMARY		
CABLE LENGTH IN MTR. 11 KV MVCC	62049 MTR.	
CABLE LENGTH BETWEEN RMU	MTR.	
CABLES		
11 KV MVCC		
POLE		
9M Steel Tubular		43-NOS.
8M PSC		00-NOS.
11M Rail Pole		00-NOS.
13M Joist		00-NOS.

DESCRIPTION	SYMBOL / QTY	
FEEDER		
JOGNINATH		
CABLE LENGTH SUMMARY		
CABLE LENGTH IN MTR. 11 KV MVCC	62049 MTR.	
CABLE LENGTH BETWEEN RMU	MTR.	
CABLES		
11 KV MVCC		
POLE		
9M Steel Tubular	≡	43-NOS.
8M PSC	≡	00-NOS.
11M Rail Pole	≡	00-NOS.
13M Joist	≡	00-NOS.

SURVEYED BY (NAME): 1. - 2. - DATE (DD/MM/YYYY):	*ALL LENGTHS ARE IN METERS	DRAWN BY: CHECKED BY: VERIFIED BY PM(SIGN & DATE):	SUBMISSION DATE: SCALE: NTS SIZE OF PAGE: A0 PAGE NO: OF
--	---------------------------------------	---	---